




**SECTION C-C'**

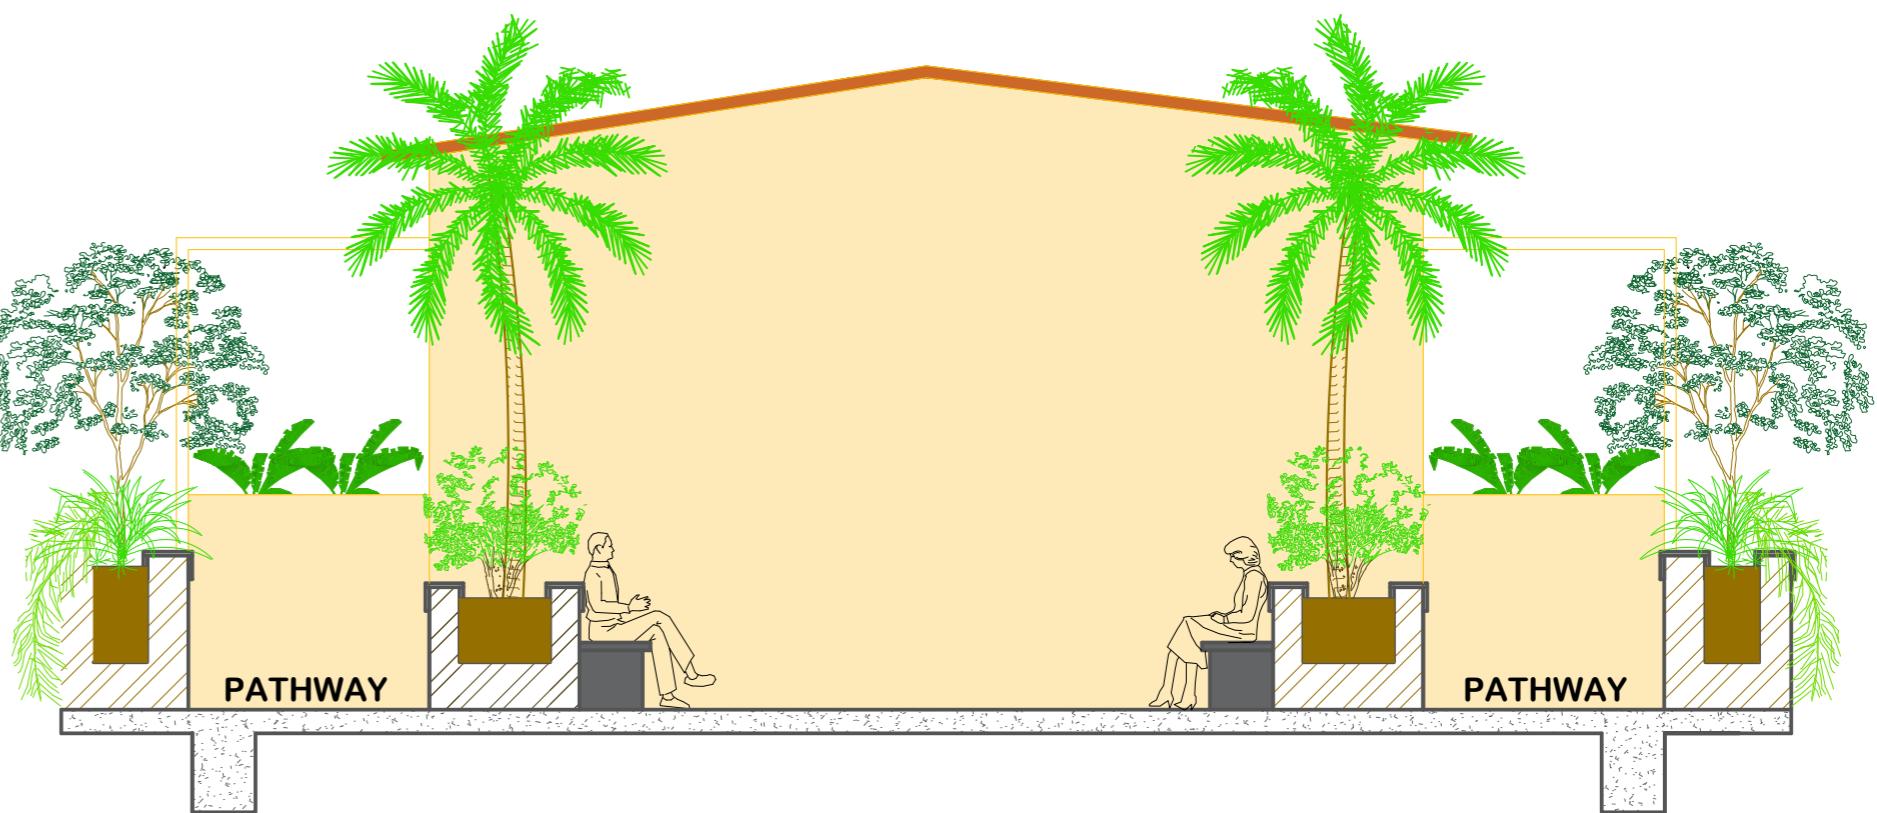


**c**

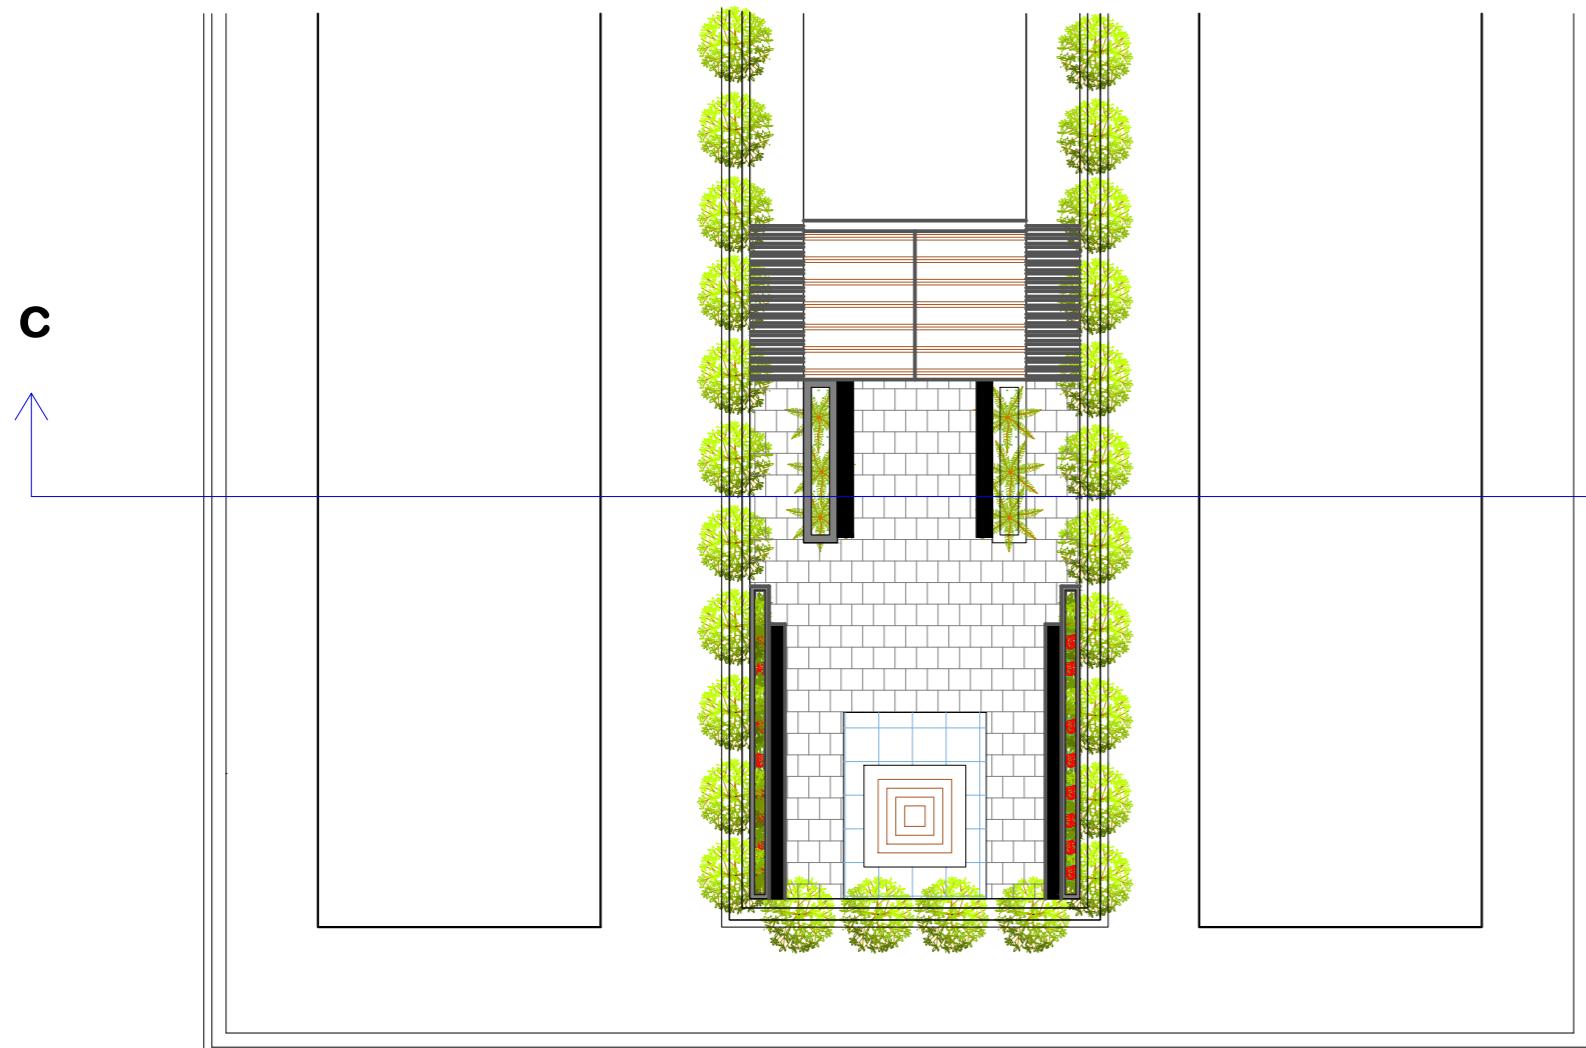


1. This space tends to **relax and calm people's mind**.
2. Mostly **elder** or aged people can be seen since it is in front of **temple** and also creates a **friendly environment**.

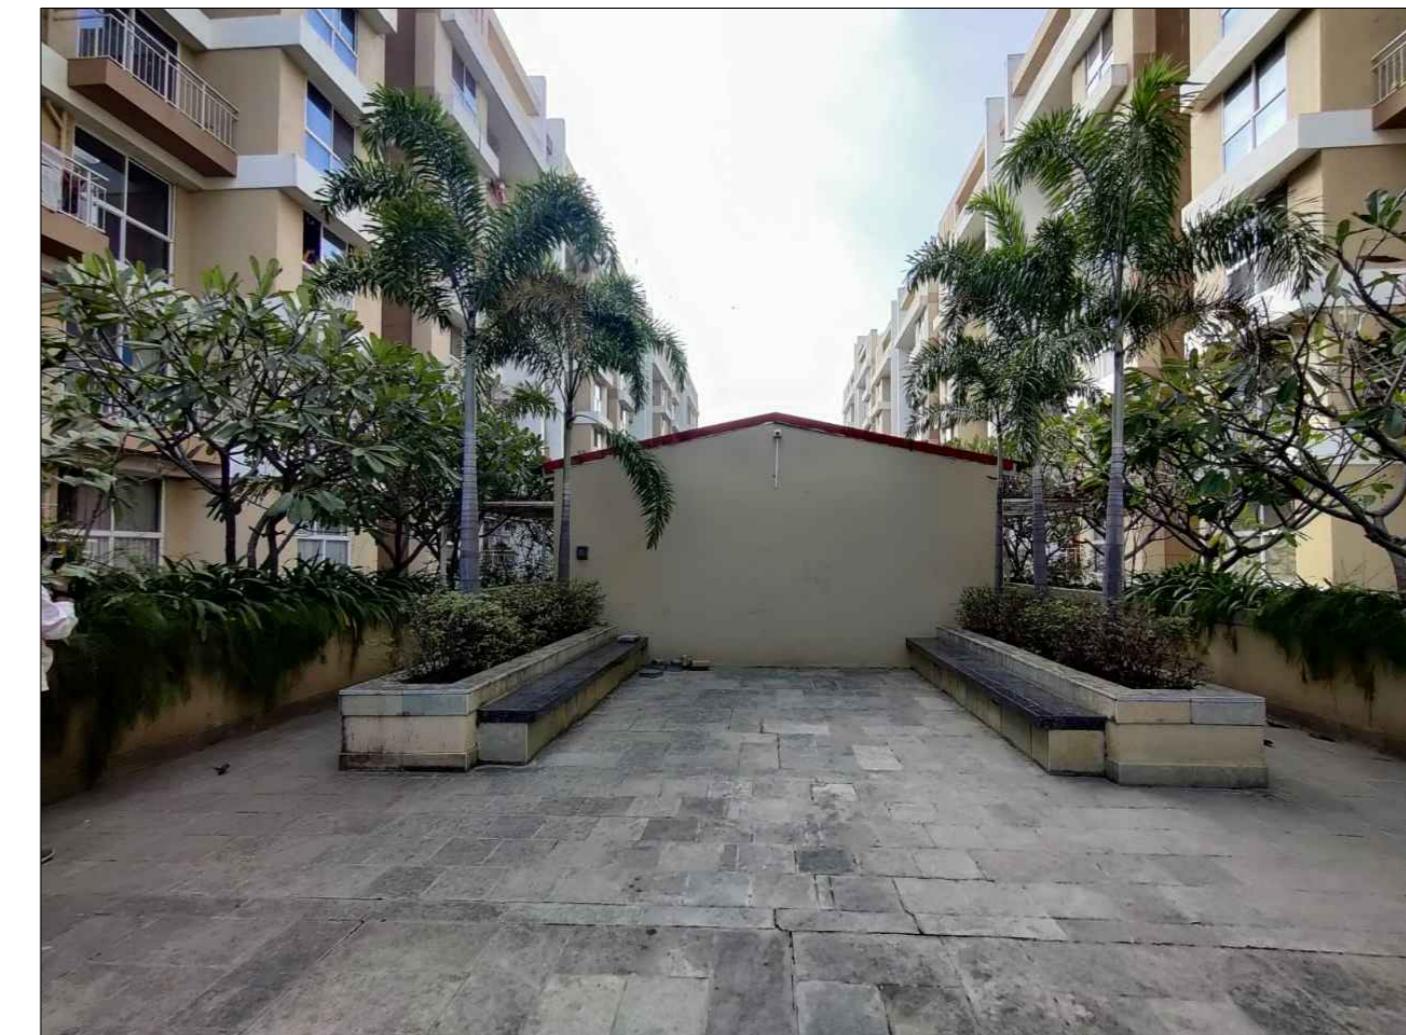

3. Different types of plants are used in this area -

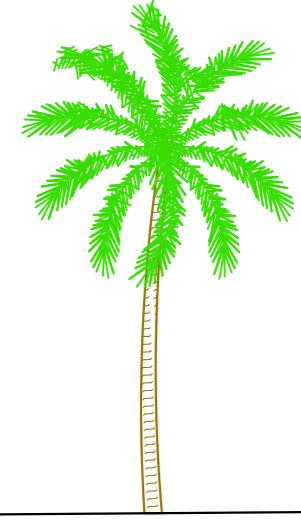

Foxtail  
Palm  
Tree

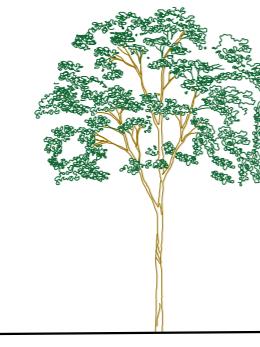

Plumeria  
Tree



Green  
Hedge




Bougainvillea  
Shrub

4. Areca palm trees have a **high ornamental value**. It provides little **shade and controls the pollution** up in the air. Their symmetrical foliage, uniformity, texture and size make them uniquely **interesting**.


5. Plumeria tree has vibrantly **colored flowers** with a **sweet fragrance** that **delights the senses**. It creates an **positive and hopeful environment**. The different parts of the plant are used traditionally to **treat various diseases**.

6. Green hedge help to **partition** the space into two different parts. They provide a **natural background** and they **can attract birds**.

7. Bougainvilleas are popular **ornamental plant**. It has breathtaking **beautiful flowers** and bright gorgeous colors. It greets you in the morning smiling and laughing and **brightens the day** and teaches us to be helpful and selfless to make others happy.

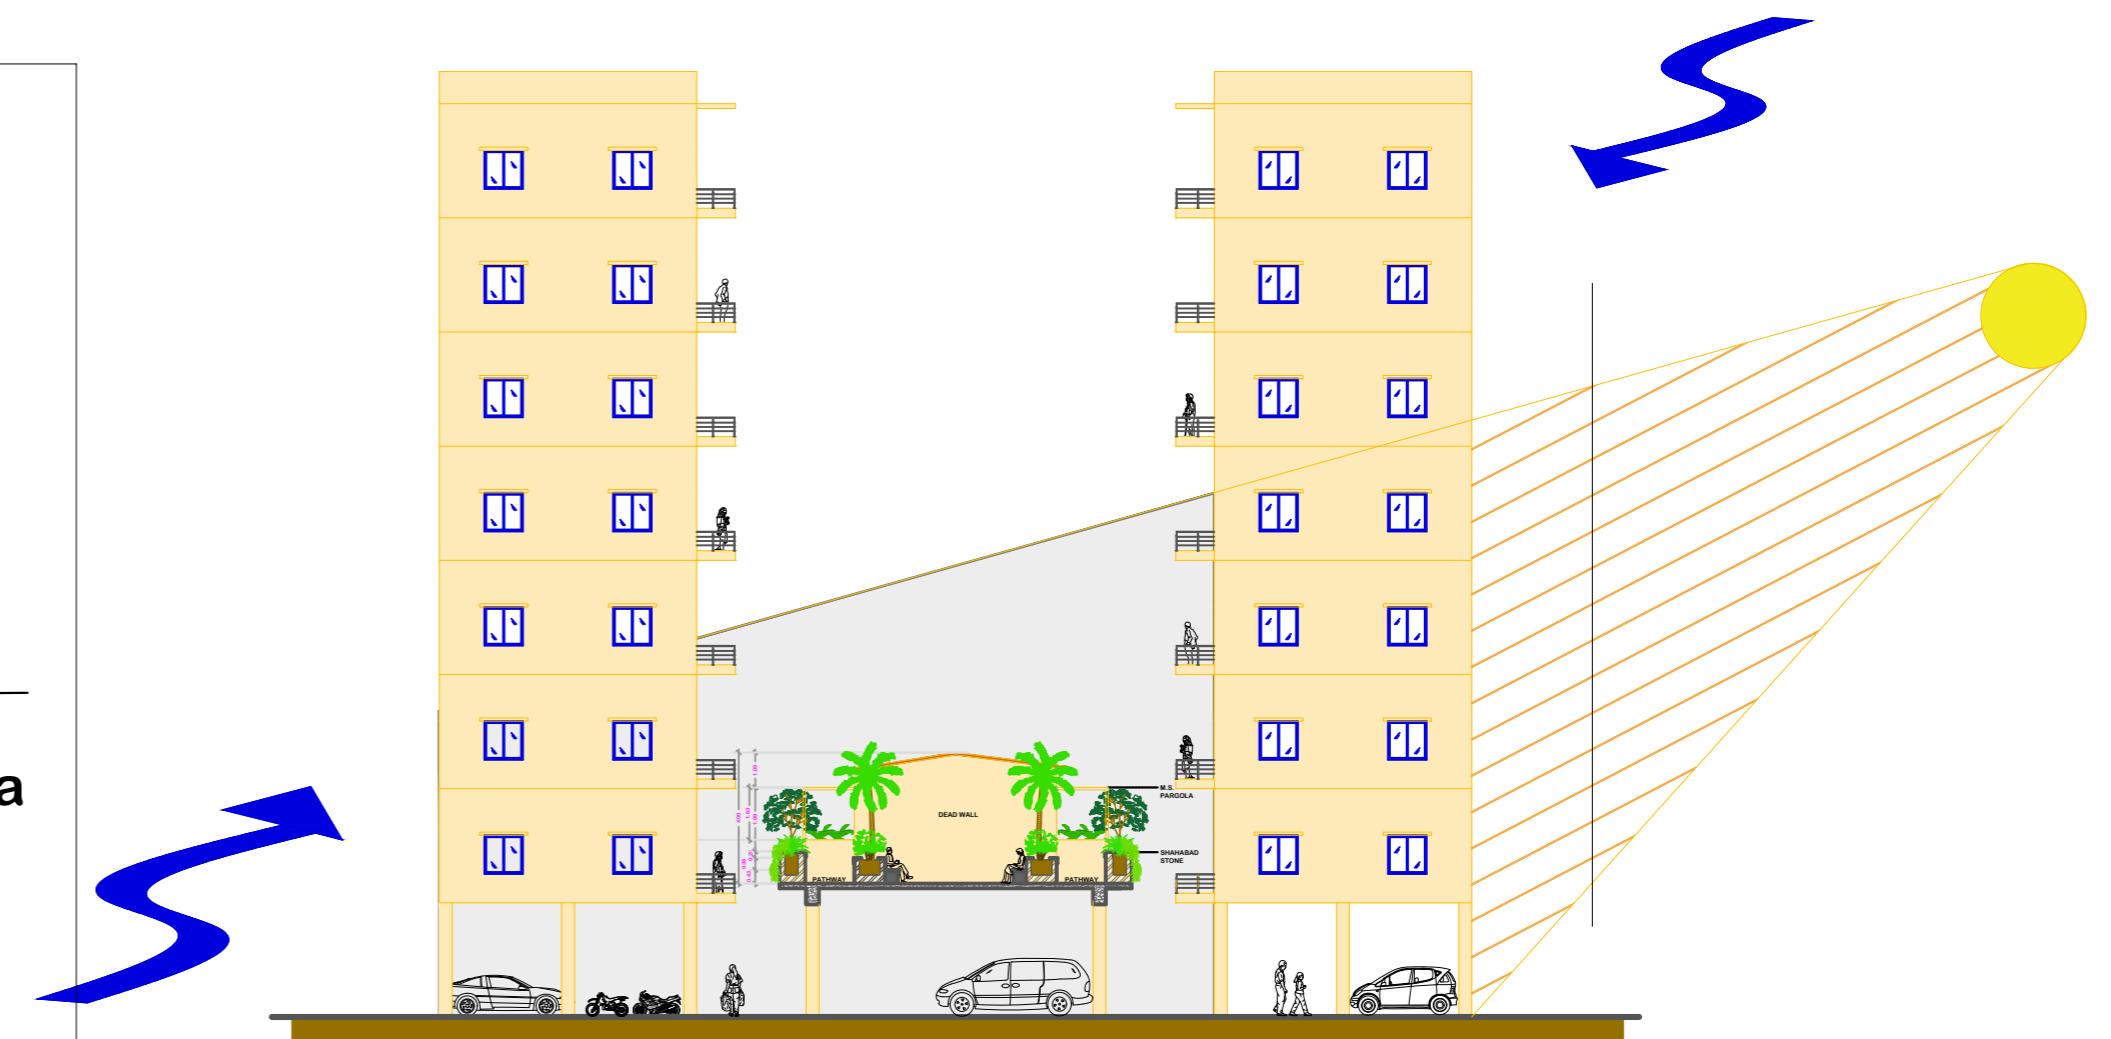

WIND FLOW, SUNLIGHT AND SHADOW

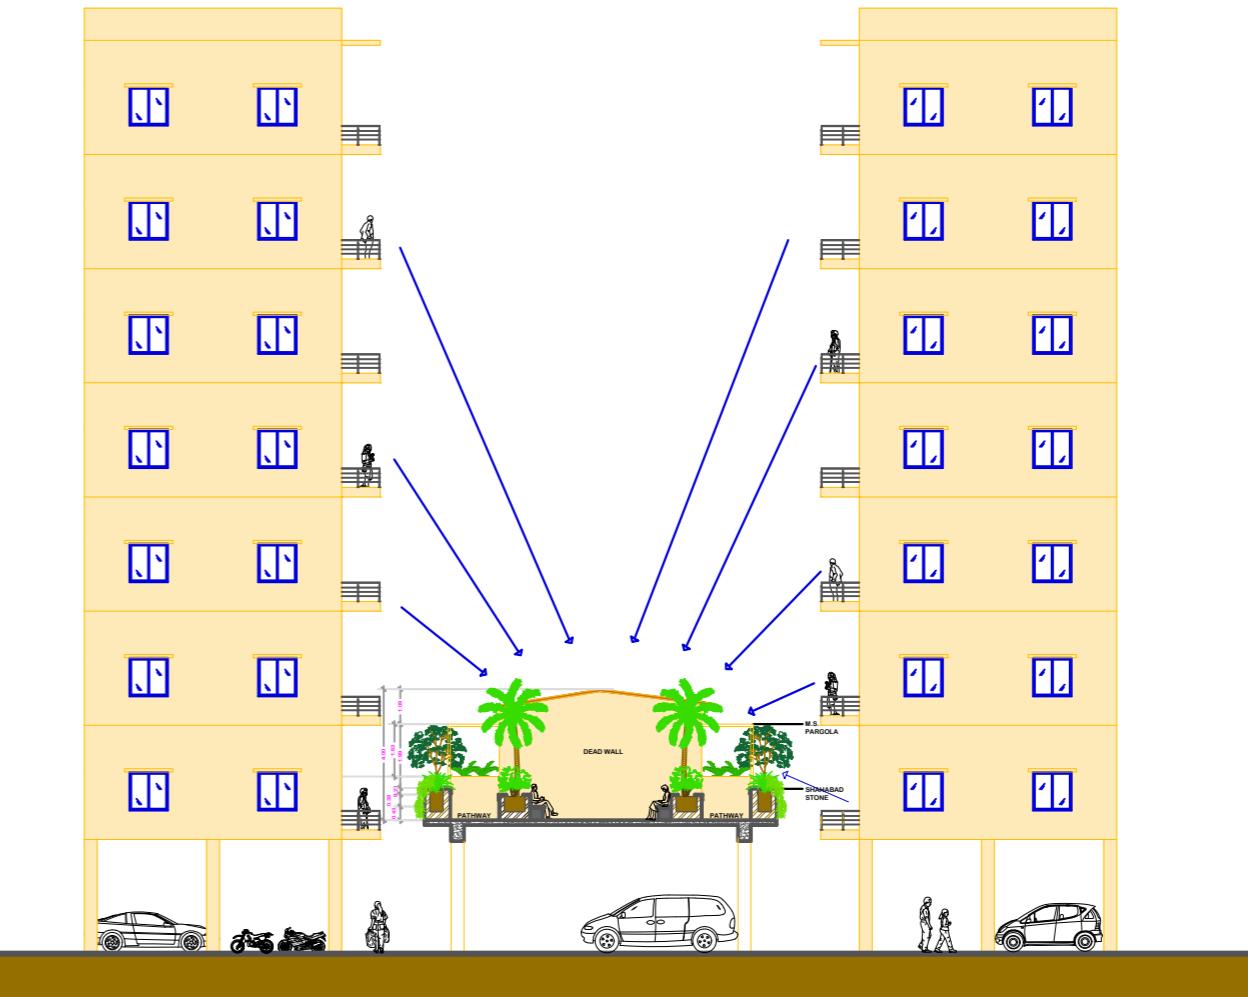

8. This is the area in front of the temple which creates a **visual connect** with the people standing/seating in the balcony.

# SITE ANALYSIS



INDIA



MAHARASHTRA



NASHIK



## SITE LOCATION -

SURVEY NO.237/1, PIMPRI ROAD, MUMBAI-AGRA NATIONAL HWY, NEAR PWD GUEST HOUSE, RAM NAGAR, IGATPURI, MAHARASHTRA- 422403




## PHYSICAL ASPECTS -

1. AREA -
2. ORIENTATION - WEST FACING
3. VEGETATION - FERTILE LAND
4. SITE LEVEL - ROAD LEVEL
5. TOPOGRAPHY - FLAT LAND
6. LANDMARKS - GOVERNMENT GUEST HOUSE, INDRUPATI TRAVELS


## FEATURES -


- 1. BUILT ROADS
- 2. GREENARY
- 3. FERTILE LAND
- 4. FRESH ENVIRONMENT
- 5. SURROUNDING AGRICULTURAL LAND

- 1. NO SERVICES NEARBY
- 2. WIND MOVEMENTS CAN HAVE AN AFFECT ON THE SITE.

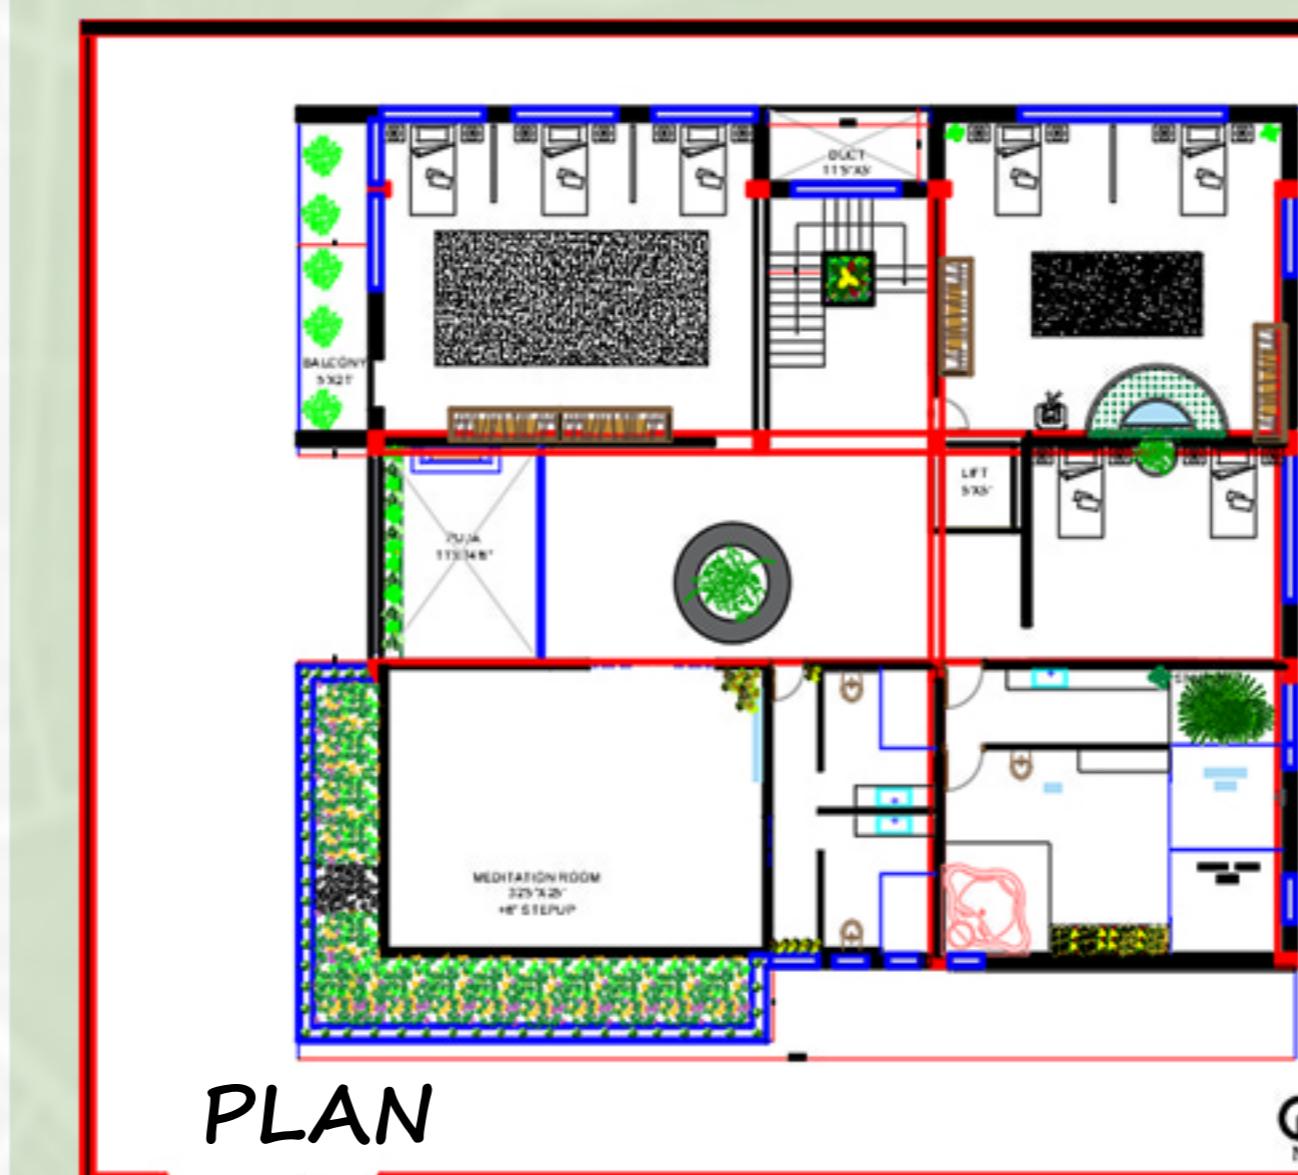


## CLIMATE AND SOIL -


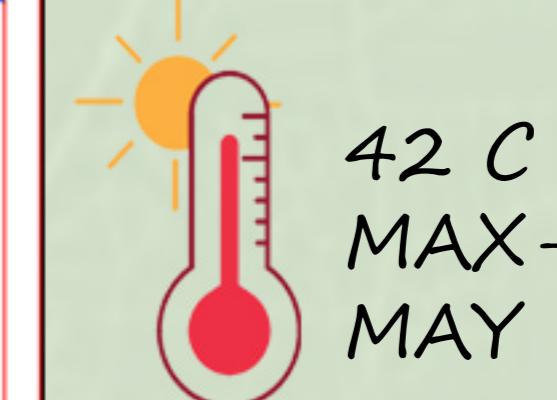


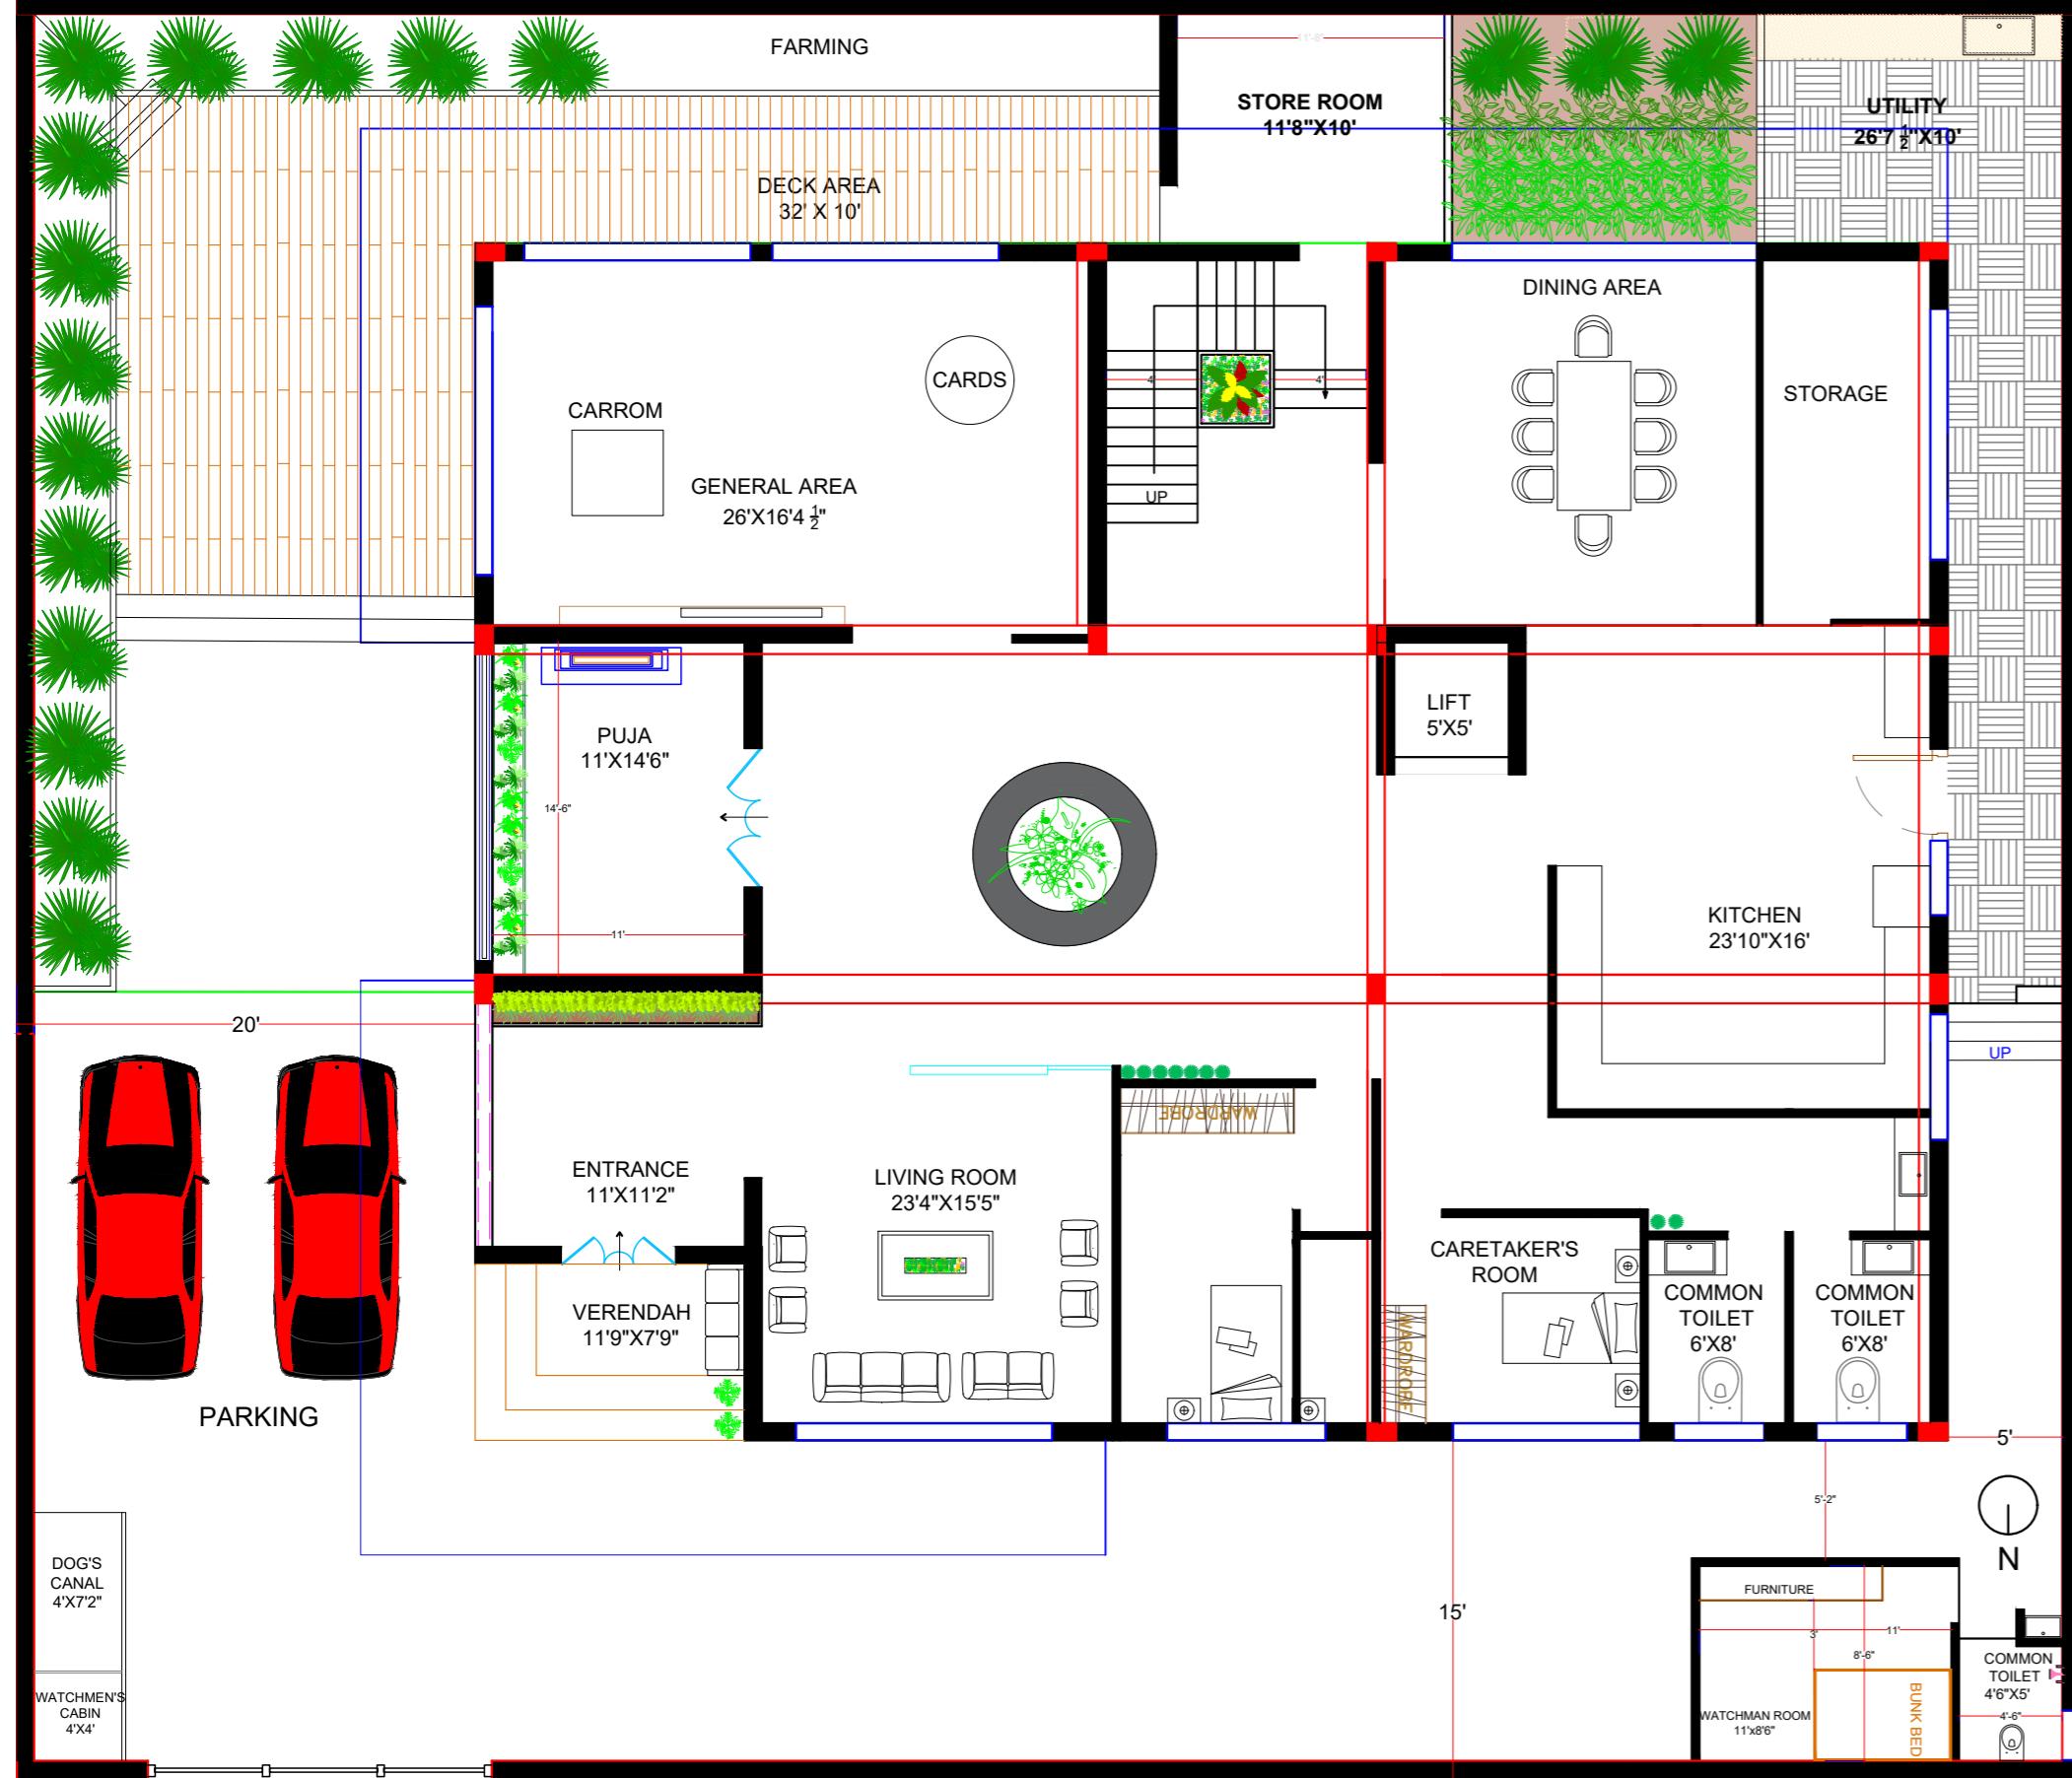

# GROUND FLOOR PLAN

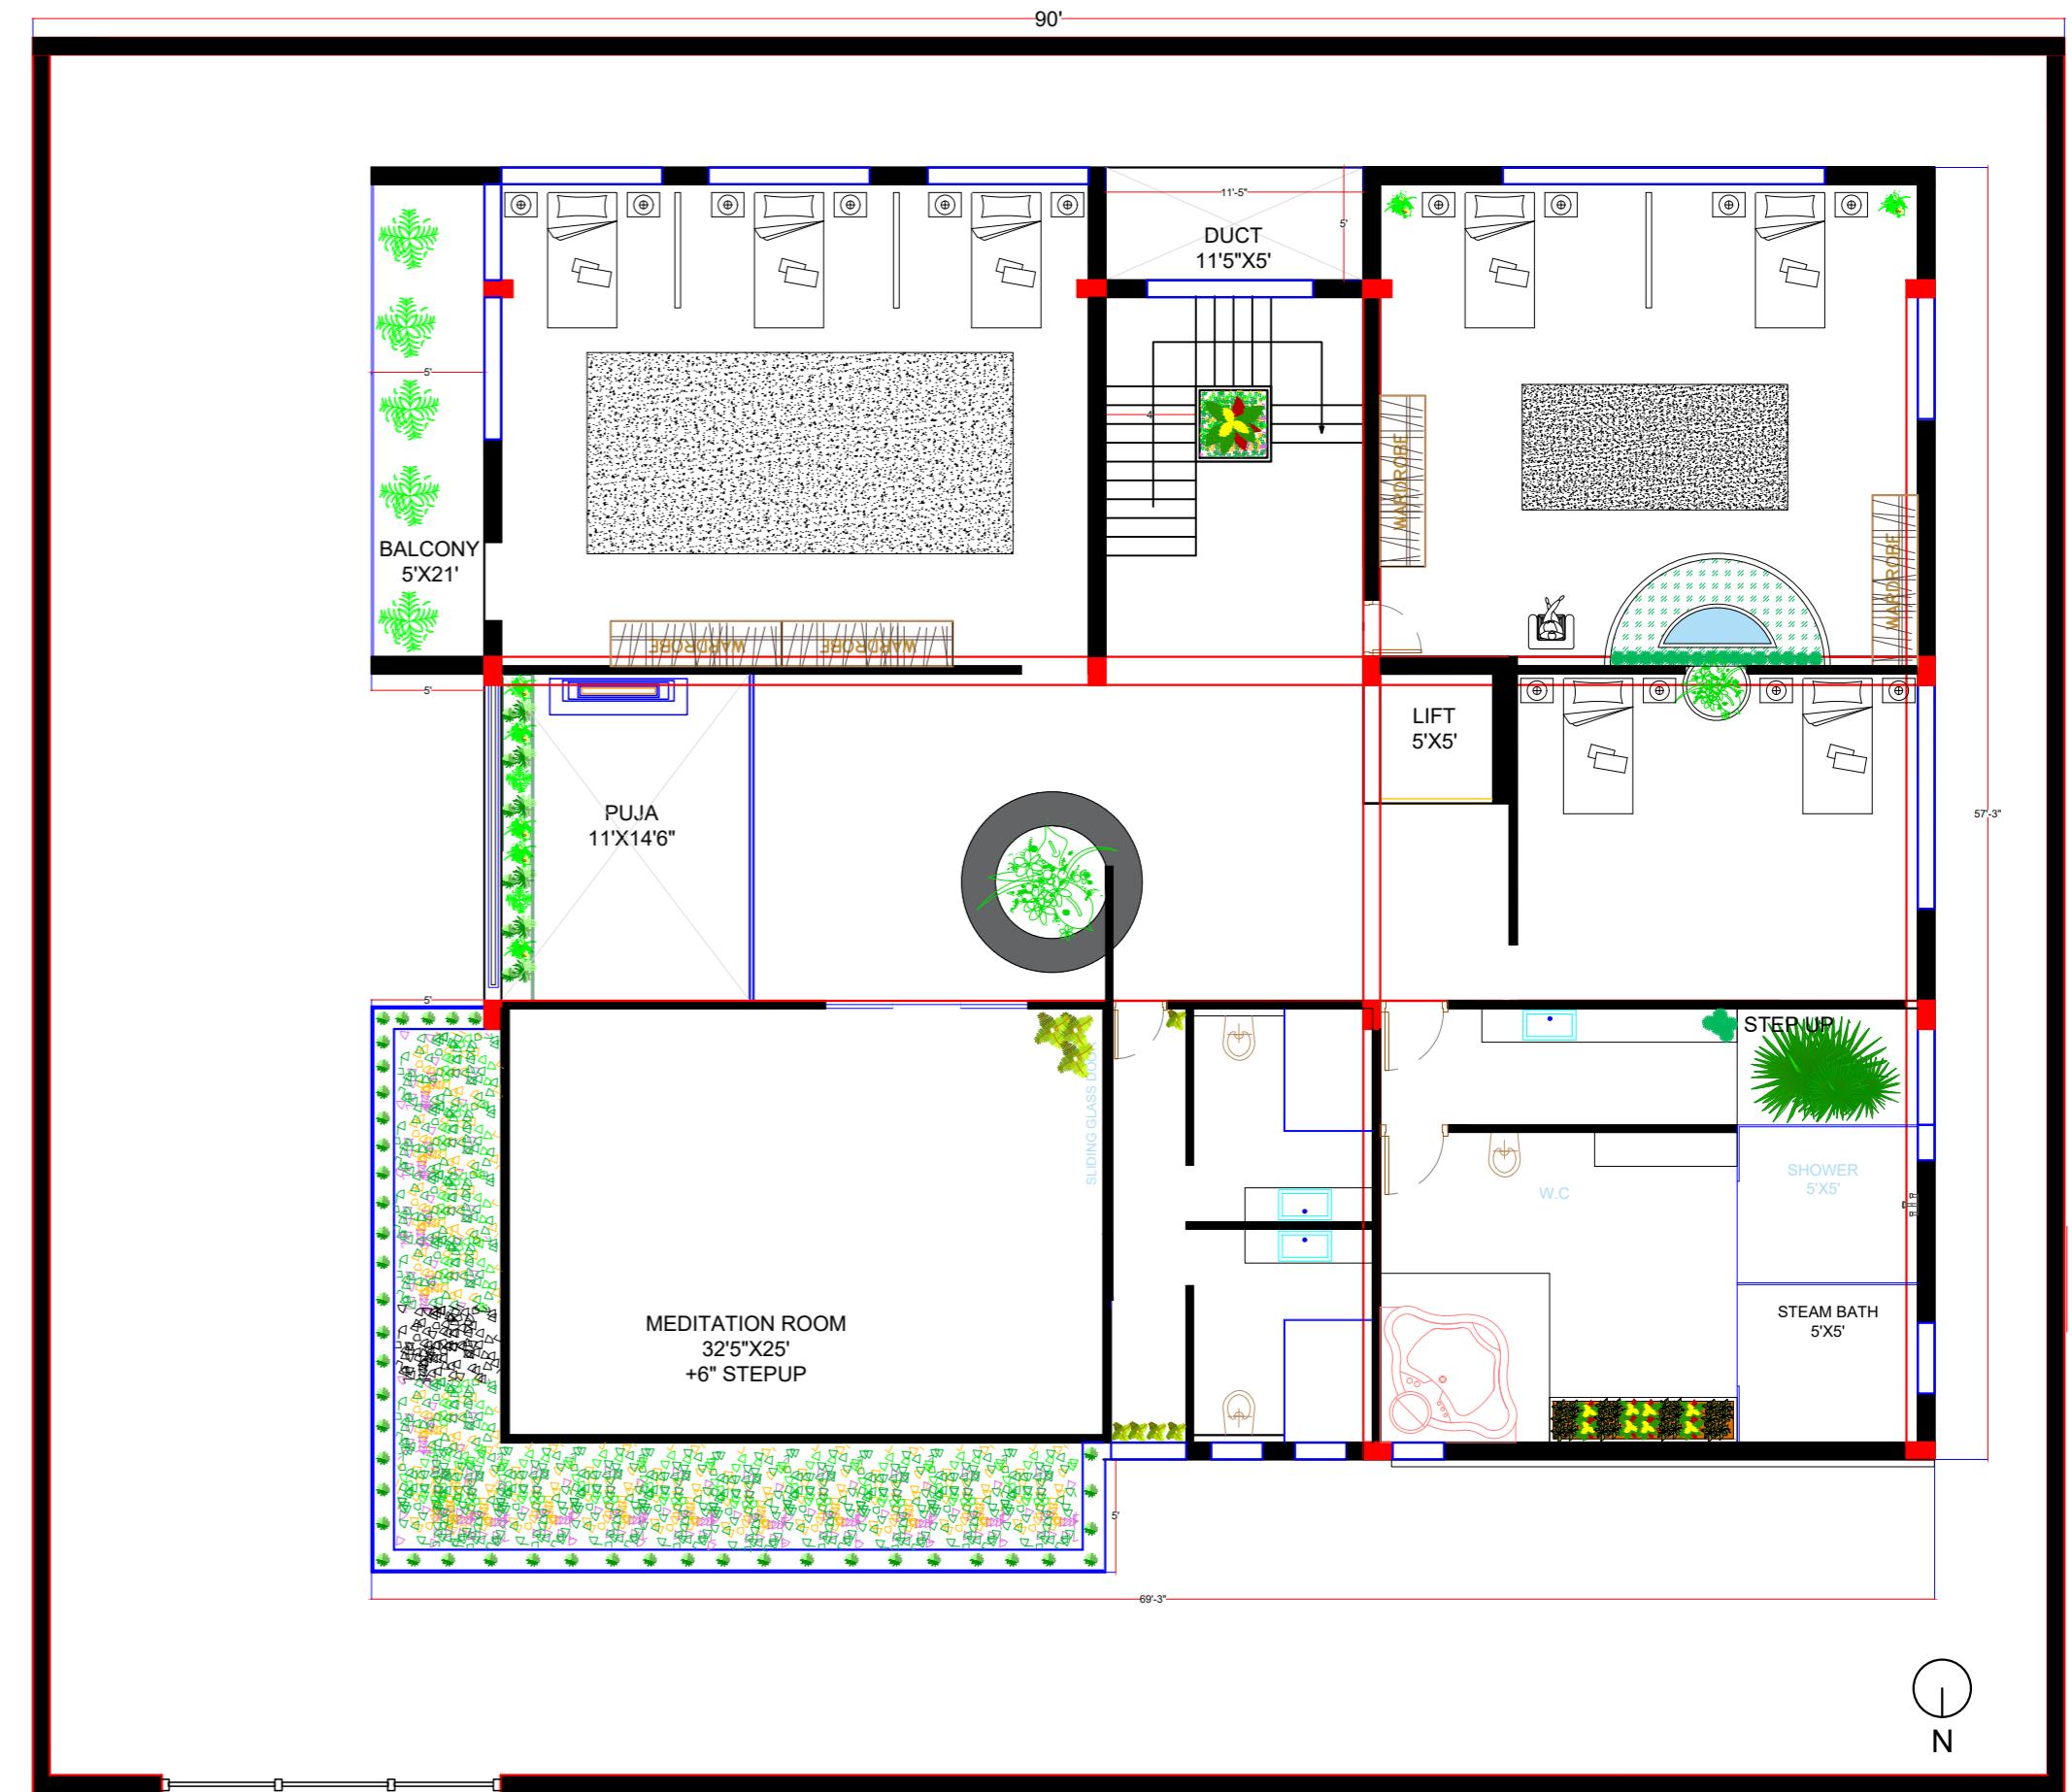

# FIRST FLOOR PLAN

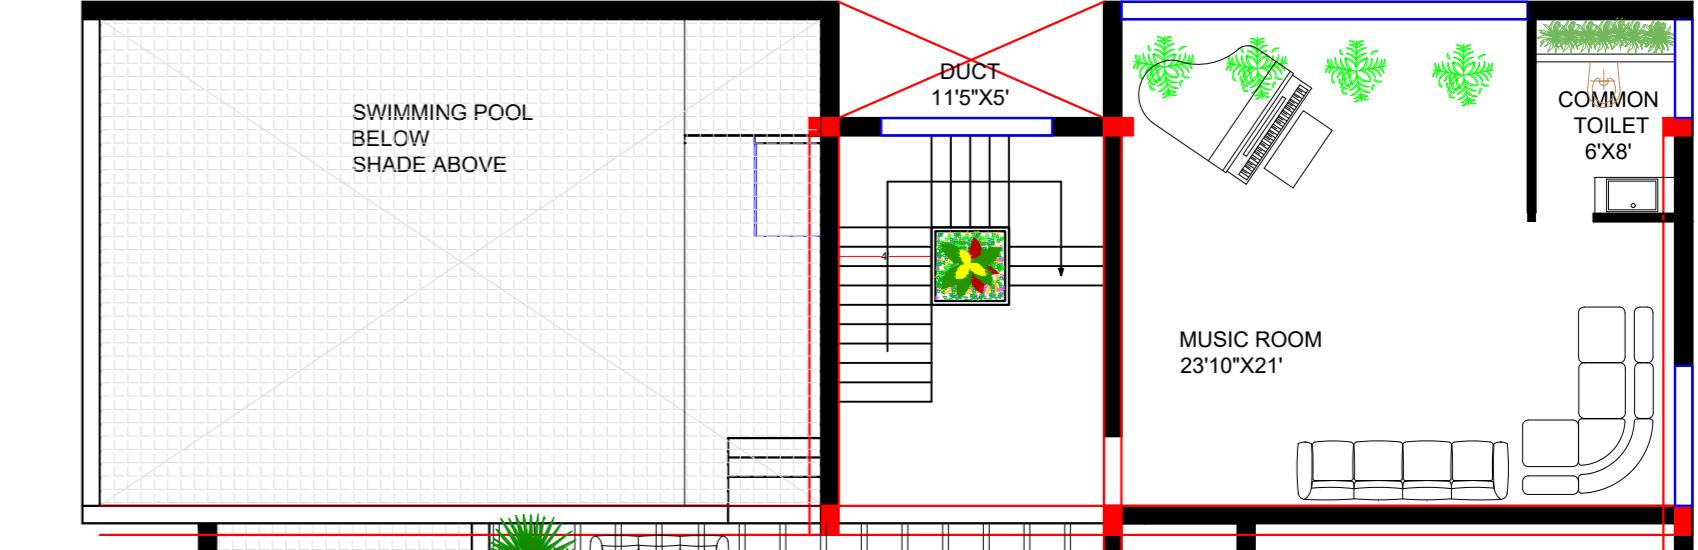
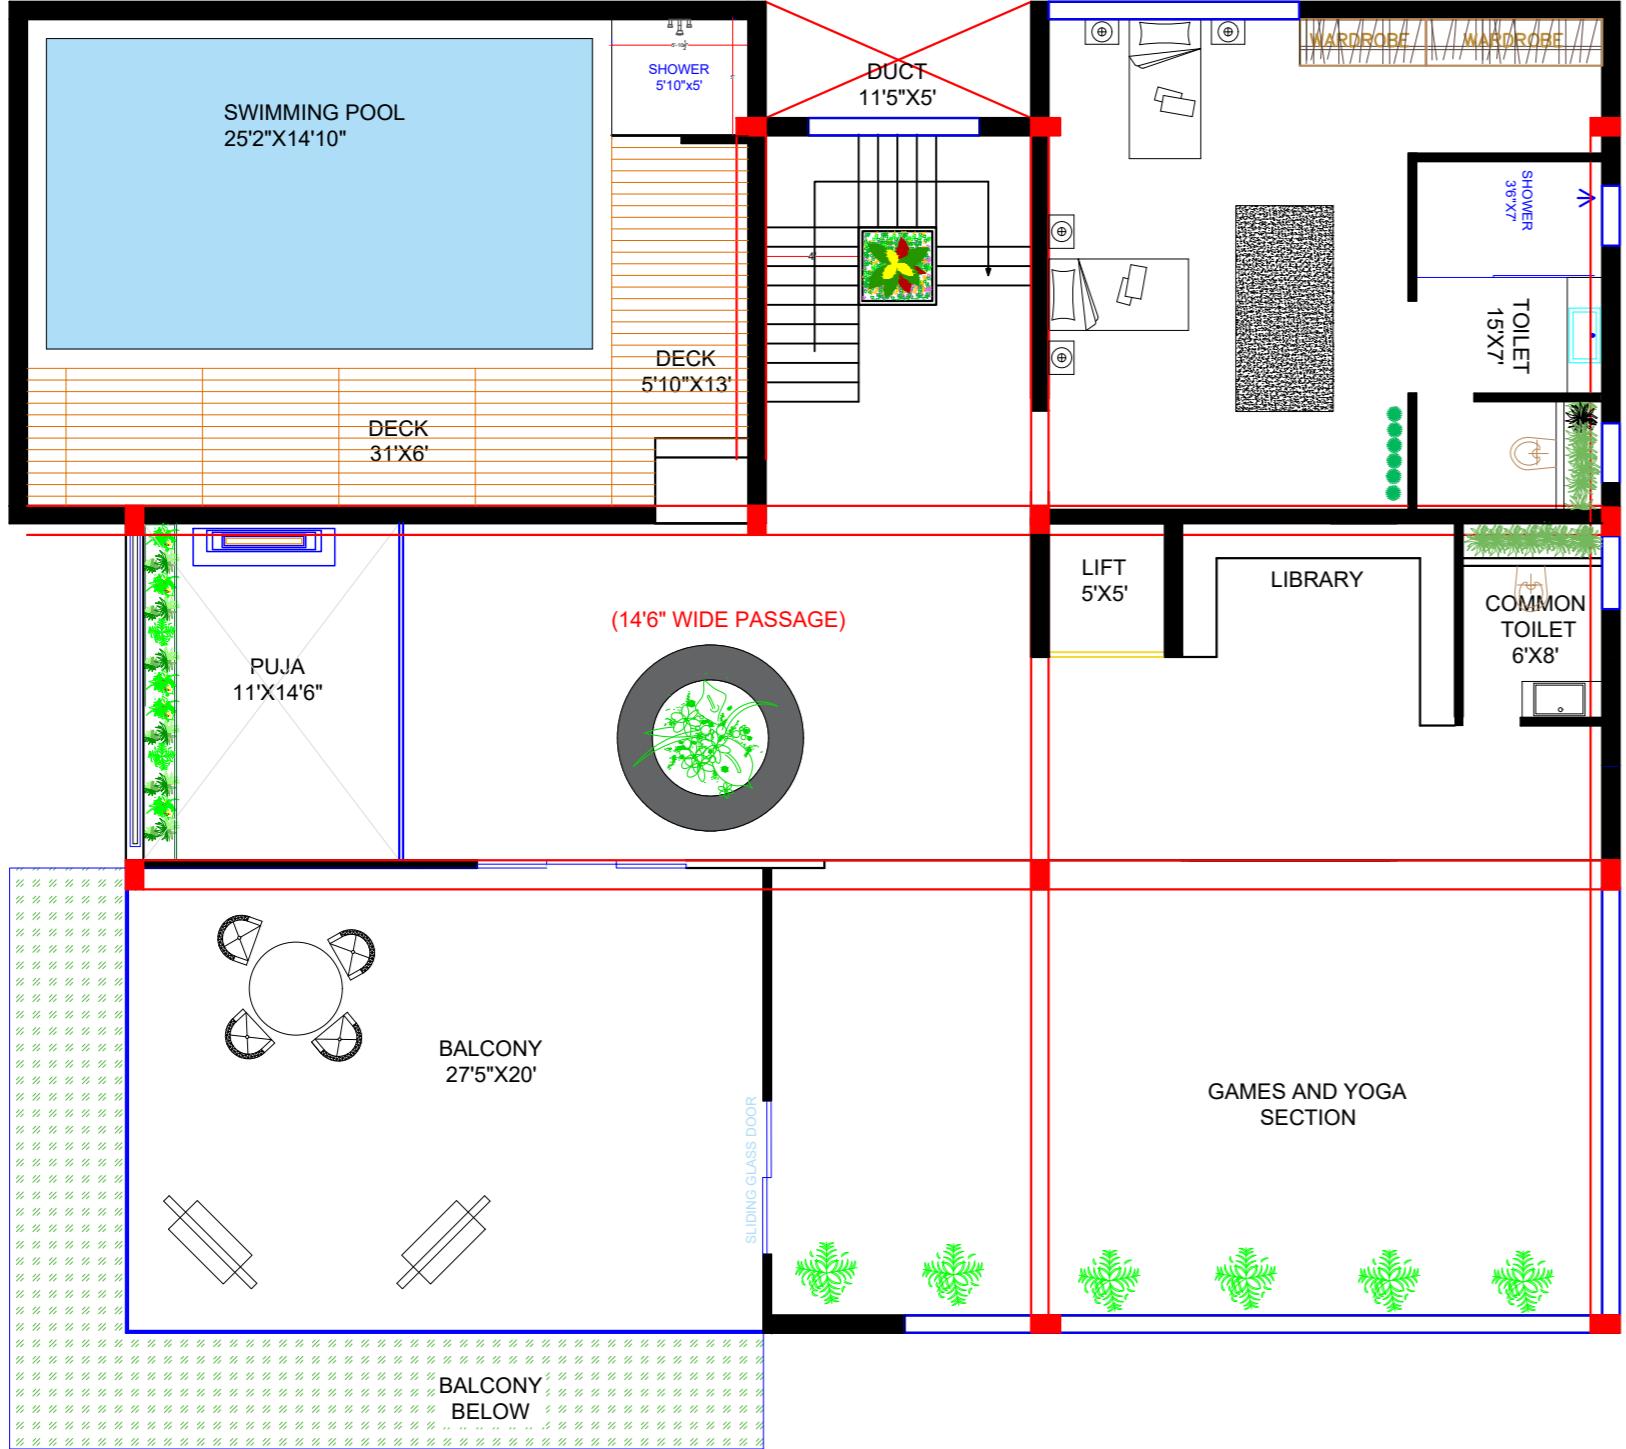


**SECOND FLOOR PLAN**

**TERRACE FLOOR PLAN**

# DETAILS

## SWIMMING POOL

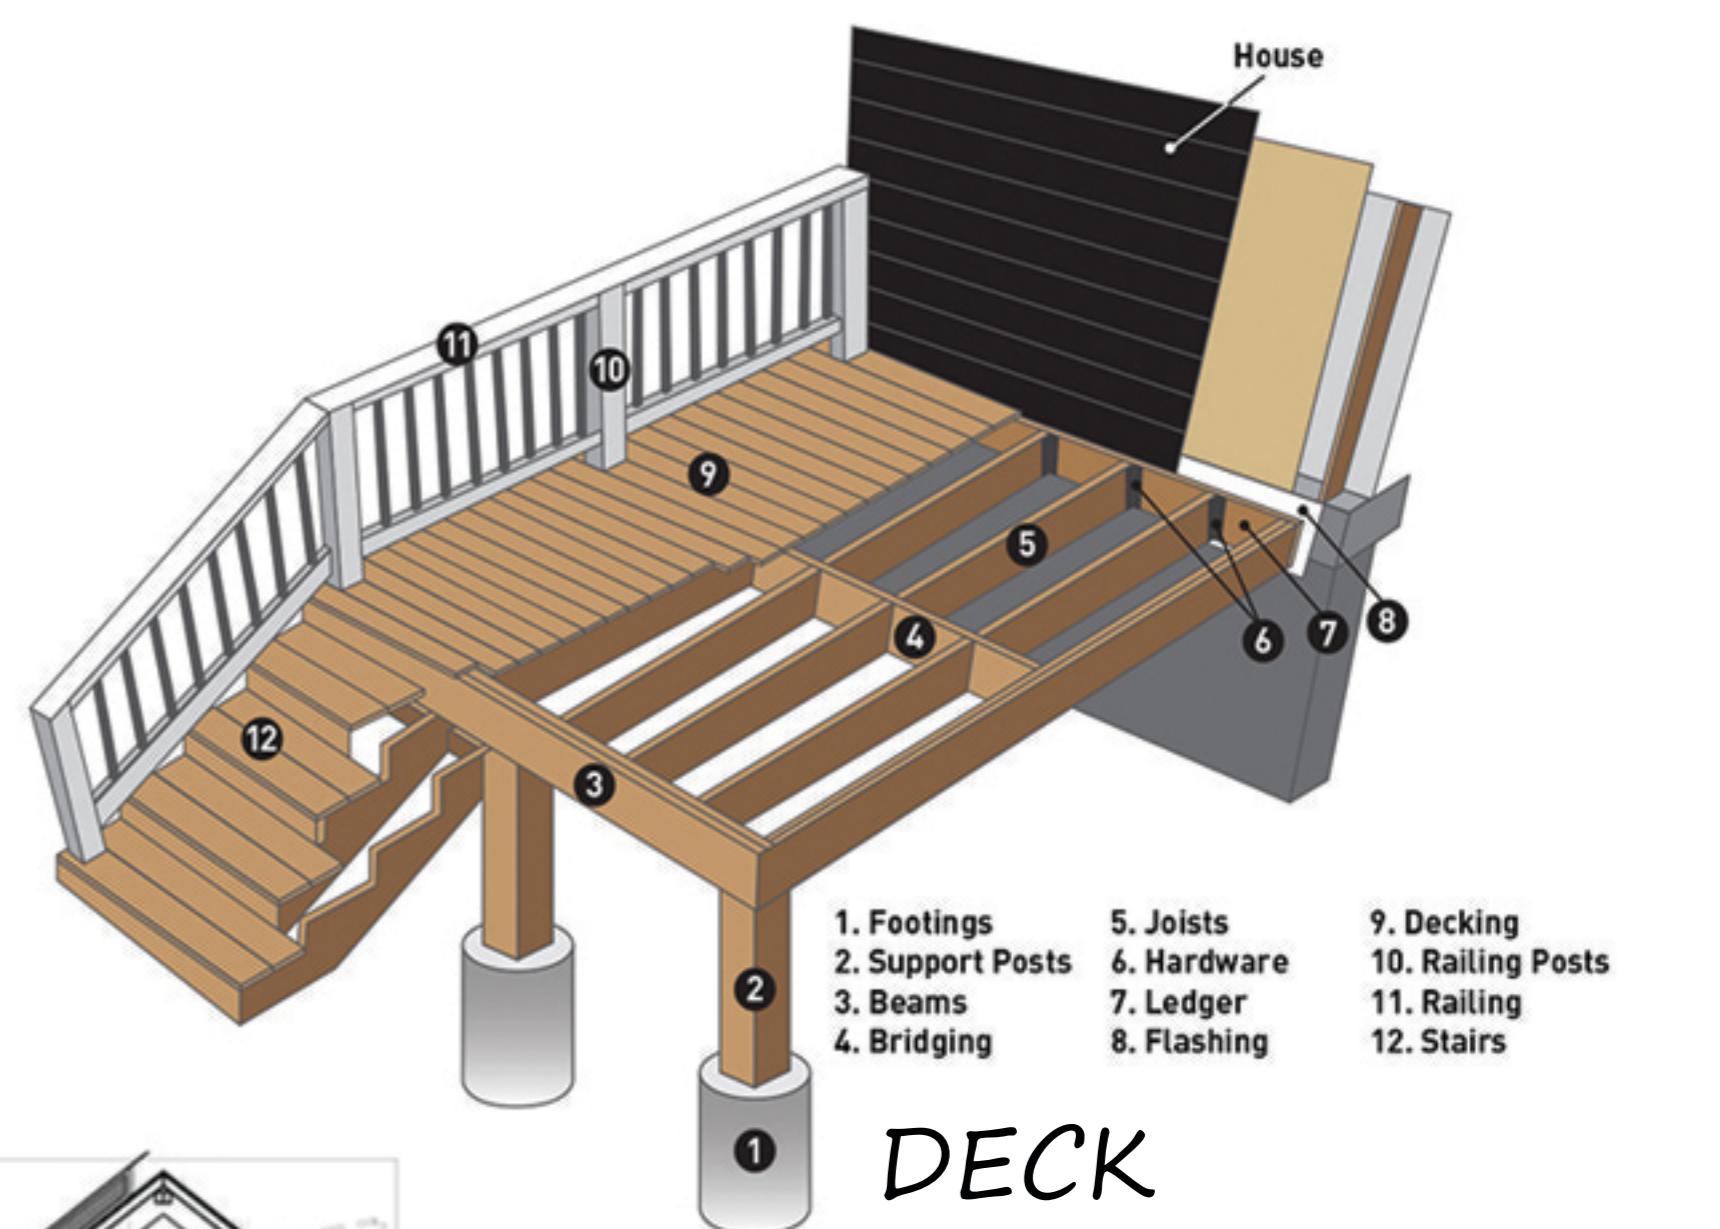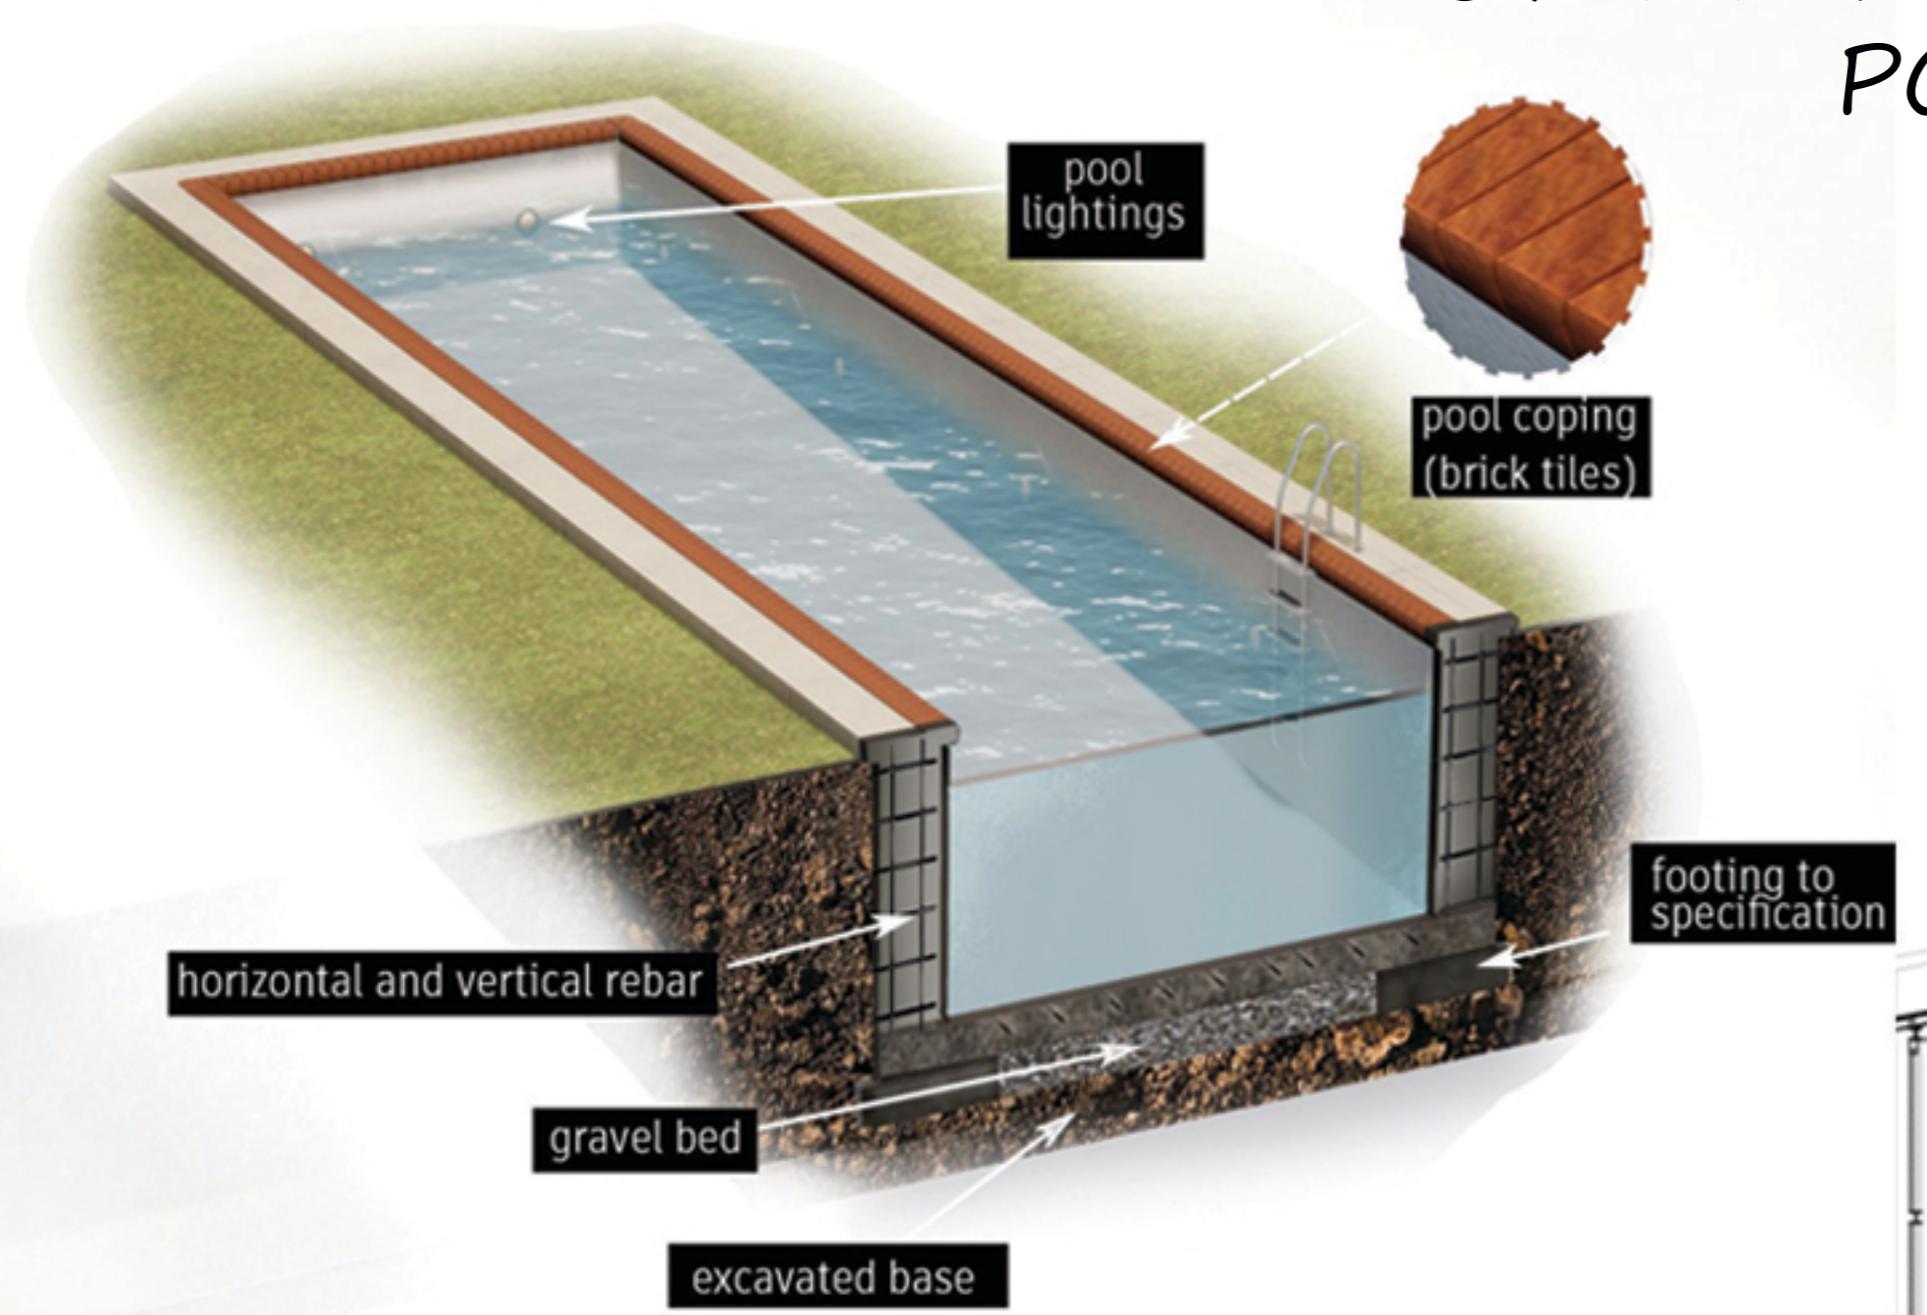


## DECK




## The Construction Details

### Planter Box

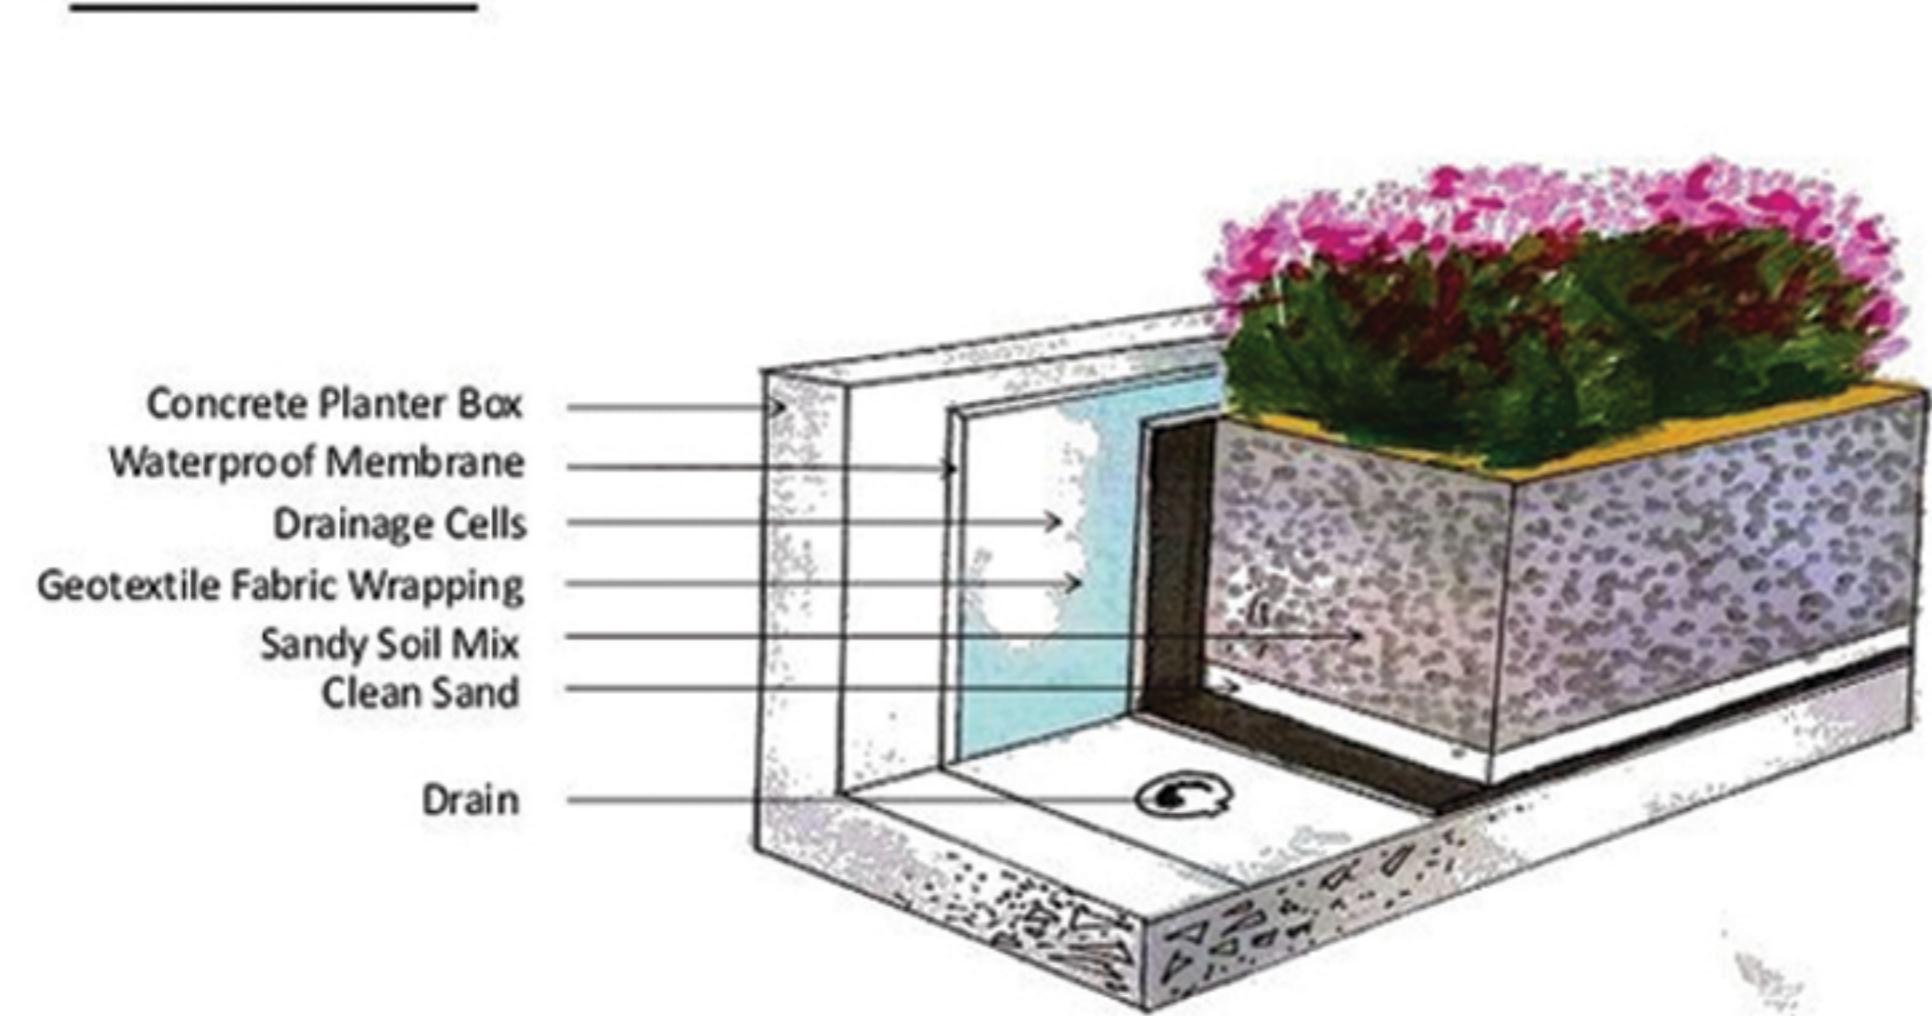

## COURTYARD

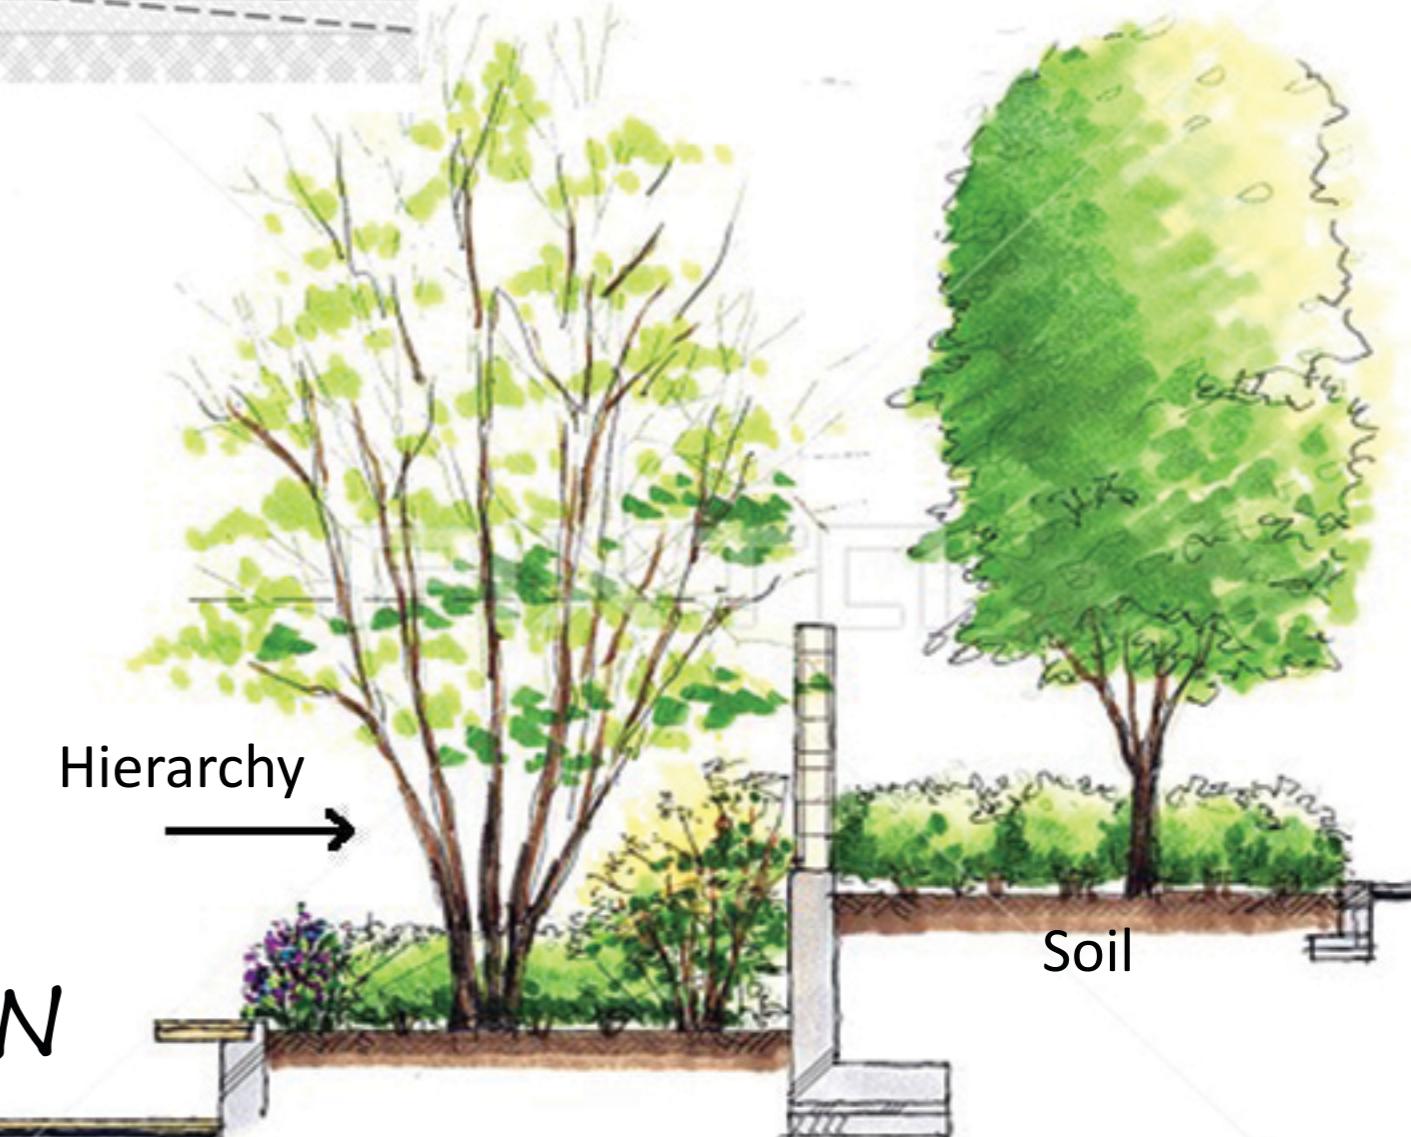

## PLANTATION

# MATERIAL BOARD



CEDAR WOOD DECK



GRANITE


OUTDOOR PORCELAIN  
TILES




PEBBLES



WOOLEN CARPET

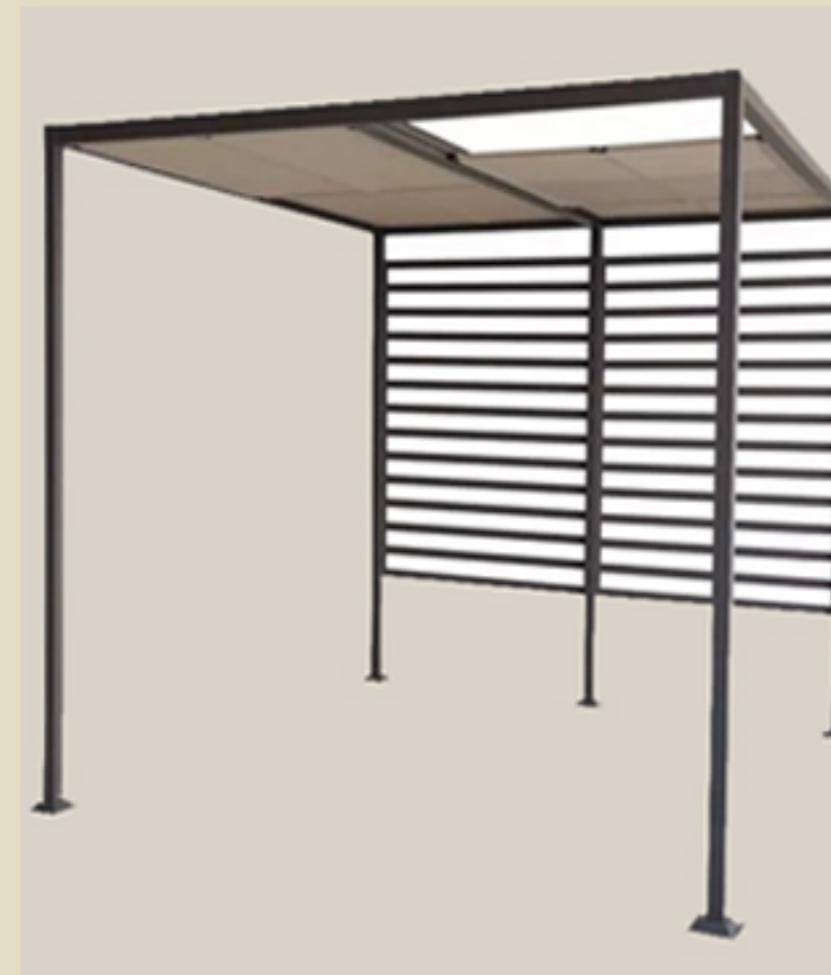

STEEL PAVILION

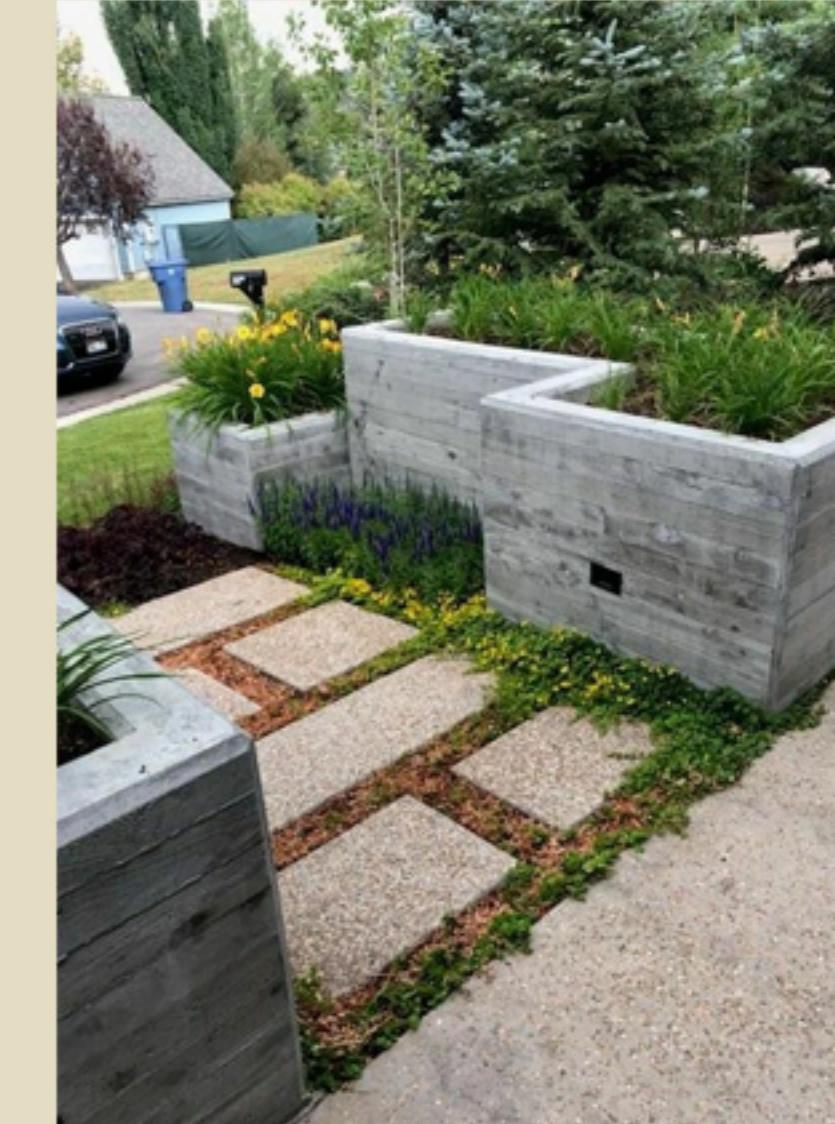


FIBERGLASS SHADE

CONCRETE

# TYPES OF PLANTS

## GROUND FLOOR

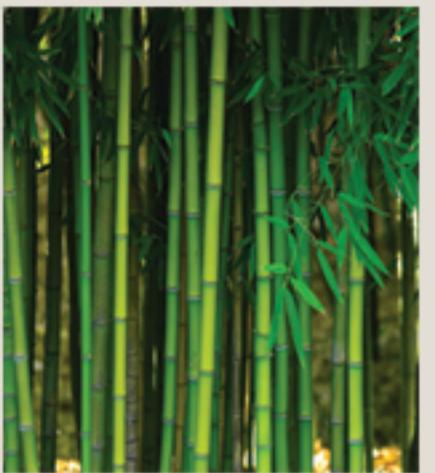

Bamboo Tree




Rose Plant



Ipomoea Shrub



Crepe myrtle Tree,  
Ophiopogon shrub

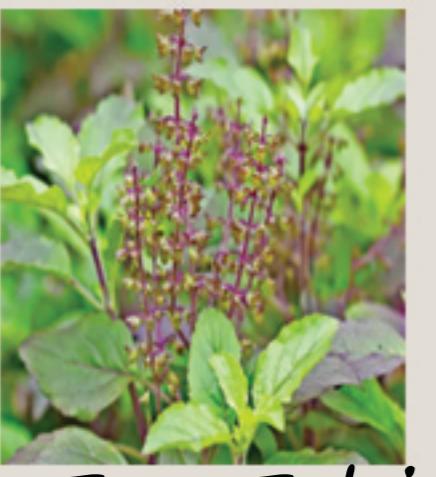

Tulsi  
Ophiopogon shrub



Lemon  
plant



Neem  
Tree



Money plant




Spider plant



Monstera plant

## SECOND FLOOR

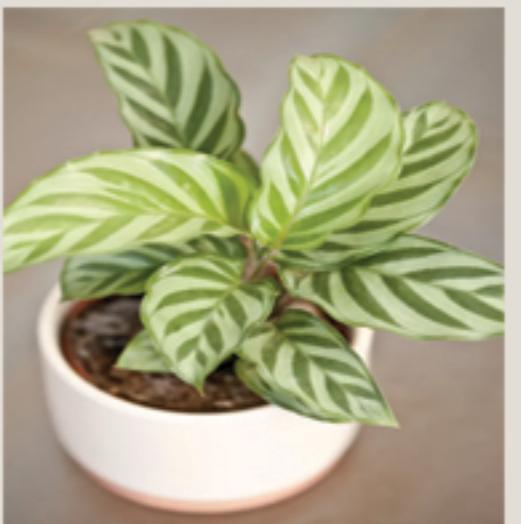

Staghornfern plant,



Bougainvillea,



Jasmine plant

## FIRST FLOOR



Bamboo plant



China palm



Areca palm  
plant

## TERRACE FLOOR



Aloe vera  
plant



Marigold  
plant



Lavender  
plant



Bougain-  
villea



Lady palm  
plant



Ixora  
plant



Jasmine  
plant



Rose  
plant